



REQUEST TO ACCESS PROPERTY - WIRELESS CARRIER

Pursuant to Annual Work Permit

Purpose: This Request is used by a wireless carrier permittee (Permittee) to obtain authorization from the appropriate Thruway Authority (Authority) Division office prior to accessing Authority property. Such access is regulated by an Authority-issued Annual Work Permit. A separate Request is required each time the property is accessed.

INSTRUCTIONS:

- Permittee:** Complete and sign Section I and send to appropriate Division Permit Office listed in Section III of this Request. Submit this Request a minimum of: 2 business days in advance of any scheduled access if Division assistance is not required; 15 business days in advance if Division assistance is required (e.g., traffic control); or 15 business days in advance if engineering or code compliance review is required. Once approved, the Permittee shall contact the Division Permit Coordinator at least 24 hours prior to accessing Authority property (48 hours if access will be outside normal business hours of 8 a.m. to 4:30 p.m., Monday through Friday) and within 24 hours of vacating the property. The approved Request must be available at the work site and provided upon request to confirm the authorization to access the specified property.
Emergency access: Submit a completed Request within 24 hours after the access. Notify the Senior Radio Dispatcher at (866) 691-8282 only if the emergency will impact the Thruway radio system. (Should a Thruway emergency exist, the Authority reserves the right to leave the radio system on or reactivate it as circumstances require.) The Permittee shall also notify all other carriers located on the tower if their systems need to be turned off.
- Division Permit Coordinator/Designee:** Review Request (send copy to Division Code Compliance Specialist, if appropriate) and complete Section II. A. If any related Authority expenses are to be waived, forward completed Request to the Division Director for approval. If related Authority expenses will not be waived, return Request to Permittee. Send copies of approved Request to: Division Traffic Operations (for notification to State Police and, when necessary, for coordination of traffic control); Office of Real Property Management and Appropriate Division Program Manager(s).
- Division Director:** If applicable, complete Section II. B. and return to Division Permit Coordinator for distribution.

Section I Permittee Information

Contact Name JACKIE DONAHUE	Email Address JDONAHUE@PHOENIXINTNL.COM	Annual Work Permit No. T3W250022	Occupancy Permit No. T3U250002
Carrier Site ID No. US-NY-2029 & 2030	Office Phone No. () -	Fax No. () -	Cell Phone No. (570) 362 - 1147
Address (local) 999 YAMATO ROAD	City BOCA RATON	State FL	Zip Code 3 3 4 3 1 -
Permittee staff, contractor or consultant entering onto Authority property:			
<u>Name</u> JACKIE DONAHUE	<u>Firm</u> PHOENIX TOWER (OWNER)	<u>Office Phone No.</u> () -	<u>Cell Phone/Pager No.</u> (570) 362 - 1147

Location [Thruway milepost(s), municipality, county]: **EXIT 37 MP 283.95 TOWN OF SALINA NY D RAMP**

Duration of scheduled access (enter specific dates): From **08252025** To **10302025**

Purpose/description of the access (attach additional sheets if necessary):

~~CONSTRUCTION OF NEW CELL TOWER @ EXIT 37 LIVERPOOL ROLLING WILLS EXCAVATING & KW SITE SERVICES, TECTONIC FOR STAKING~~

List all motorized equipment/vehicles to be used:

~~SERVICE TRUCKS, EXCAVATORS, ETC. KIA TELLURIDE~~

Is it anticipated that private traffic control will be required? ☐ Yes ☒ No

Is support from Authority Division staff being requested? ☐ Yes, describe below. ☒ No

Affirmation: The undersigned certifies that the above information is correct.

Jackie Donahue
Permittee Authorized Signature

08252025
Date

REQUEST TO ACCESS PROPERTY - WIRELESS CARRIER
Pursuant to Annual Work Permit

Annual Work Permit No. T3W250022
Occupancy Permit No. T3U250002

Section II Approvals

A. Division Permit Coordinator/Designee

Authorization to access Authority property as defined in this Request is: ☒ Approved ☐ Disapproved

Comments/Conditions: As per conditions of NYSTA permits T3W250022 & T3U250002. Access from mainline shall
comply with attached WZTC conditions. Below is a link to the NYSTA Standard Sheets for reference.

<https://www.thruway.ny.gov/business/contractors/standard-sheets/may-01-2025-vol1.pdf>

Trevor Thieme

Trevor Thieme

9/2/2025

Division Permit Coordinator/Designee Name (print name)

Division Permit Coordinator/Designee Signature

Date

NOTE: If any related Authority expenses are to be waived, forward to Division Director for approval (list expenses in "Comments" above).

B. Division Director (in consultation with appropriate Authority managers)

Waive payment for relevant Authority expenses: ☐ Approved ☐ Disapproved

Comments/Conditions: _____

Division Director Name (please print)

Division Director Signature

Date

Section III Division Permit Offices

NYS Thruway Authority
New York Division
Division Permit Coordinator
4 Executive Blvd.
Suffern, NY 10901
Phone: (845) 918-2510
Fax: (845) 918-2596

NYS Thruway Authority
Albany Division
Division Permit Coordinator
P.O. Box 861
Albany, NY 12201-0861
Phone: (518) 436-2710
Fax: (518) 436-2932

NYS Thruway Authority
Syracuse Division
Division Permit Coordinator
290 Elwood Davis Rd., Suite 250
Liverpool, NY 13088-2103
Phone: (315) 438-2420
Fax: (315) 461-0765

NYS Thruway Authority
Buffalo Division
Division Permit Coordinator
455 Cayuga Rd., Suite 800
Cheektowaga, NY 14225
Phone: (716) 631-9017
Fax: (716) 626-5362

DIVISION LIMITS

New York

- Mainline - mileposts: 0.00 - 76.50
- Garden State Parkway Connection: GS 0.00 - GS 2.40
- New England Section: NE 0.17 - NE 15.01
- I-287 Cross Westchester: CWE 0.00 - CWE 10.90

Albany

- Mainline - mileposts: 76.50 - 197.90
- Berkshire Section: B 0.00 - B 24.28

Syracuse

- Mainline - mileposts: 197.90 - 350.60

Buffalo

- Mainline - mileposts: 350.60 - 496.00
- Niagara Section: N 0.00 - N 21.50

1. All work will require notification to and approval by the Division Permit Coordinator at (315) 438-2391 at least 2 business days prior to the start of work. Specific operations may require site and/or operation plans prior to approval.

2. All contractor personnel working on our right-of-way shall observe all Authority rules and regulations and are required to wear a hard hat and High Visibility Safety apparel that meets Performance Class 3 requirements of the ANSI/ISEA 107-2004 publication entitled "American National Standard for High-Visibility Safety Apparel and Headwear".

3. Appropriate Work Zone Traffic Control (WZTC) is to be utilized when necessary. Encroachment of a travel lane is not allowed. Our Traffic Operations Department must approve any traffic control.

a. Entry to the mainline is not allowed from the project site, all vehicles must exit through the interchange before re-entering the mainline.

b. The following NYSTA Standard Sheets (attached) shall be used while accessing the project site from the mainline:

i. TA 619-06 (Option B) anytime vehicles will be accessing the site

ii. TA 619-04 while unloading equipment on the shoulder or working within 30 feet of the white line for less than 2 hours

iii. TA 619-03 working within 30 feet of the white line for more than 2 hours

4. All vehicles used on our system must be equipped with a rotating amber light, which is to be used when parked. Vehicles must be parked off the pavement. No personal vehicles are allowed on Thruway ROW.

5. All work is dependent upon weather conditions. No work is to be performed during periods of adverse weather.

6. No other contract work, demolition, destruction, or construction work is authorized by this access.

7. Toll free use or U-turns on the Thruway System are not authorized by this Access. A written request must be submitted to our Traffic and Safety Department to obtain authorization for U-turns (p. 17, section 6, of the NYSTA Occupancy and Work Permit Accommodation Policy booklet).

8. All personnel within NYSTA right-of-way shall be familiar with and abide by the attached documents; "Working within Thruway Right-of-Way" and "Occupancy and Work Permit Accommodation Guidelines TAP-401".

TABLE NY1-A BARRIER VEHICLE USE REQUIREMENTS (LONG TERM, INTERMEDIATE TERM & SHORT TERM STATIONARY CLOSURES)				
CLOSURE TYPE	EXPOSURE CONDITION ¹	USE REQUIREMENTS ^{4, 5}		
		FREEWAY	NON-FREEWAY (PRECONSTRUCTION POSTED SPEED LIMIT)	
			≥ 45 MPH	35-40 MPH ≤ 30 MPH
LANE CLOSURE	WORKERS ON FOOT OR IN VEHICLES EXPOSED TO TRAFFIC	REQUIRED ³	REQUIRED ³	REQUIRED ³ OPTIONAL ²
	NON-TRAVERSABLE HAZARD (E. EQUIPMENT, MATERIALS, EXCAVATION) ONLY NO WORKERS EXPOSED	REQUIRED ³	REQUIRED ³	OPTIONAL ² OPTIONAL ²
SHOULDER CLOSURE	WORKERS ON FOOT OR IN VEHICLES EXPOSED TO TRAFFIC	REQUIRED ³	REQUIRED ³	OPTIONAL ² OPTIONAL ²
	NON-TRAVERSABLE HAZARD (E. EQUIPMENT, MATERIALS, EXCAVATION) ONLY NO WORKERS EXPOSED	REQUIRED ³	OPTIONAL ²	OPTIONAL ² OPTIONAL ²

1. THE EXPOSURE CONDITIONS DESCRIBED IN TABLE NY1-A ASSUMES THERE IS NO POSITIVE PROTECTION (TEMPORARY TRAFFIC BARRIER) PRESENT. WHERE WORKERS OR HAZARDS ARE PROTECTED BY A TEMPORARY TRAFFIC BARRIER, BARRIER VEHICLES ARE NOT REQUIRED.
2. WHERE THE REQUIREMENT IS "OPTIONAL", EITHER A BARRIER VEHICLE OR THE STANDARD LONGITUDINAL BUFFER SPACE (TABLE 6C-2) SHALL BE PROVIDED.
3. REQUIREMENTS SHALL INCLUDE PROVIDING A SEPARATE BARRIER VEHICLE FOR EACH CLOSED LANE AND EACH CLOSED SHOULDER 8 FEET OR GREATER IN WIDTH. IF THE WORK SPACE MOVES WITHIN THE STATIONARY CLOSURE, THE BARRIER VEHICLE SHALL BE REPOSITIONED ACCORDINGLY. BARRIER VEHICLES PROTECTING NON-TRAVERSABLE HAZARDS SHALL REMAIN IN PLACE DURING BOTH WORKING AND NON-WORKING HOURS UNTIL THE HAZARD NO LONGER EXISTS. EXCEPTIONS TO THESE REQUIREMENTS MAY BE MADE BY THE ENGINEER, WHERE BARRIER VEHICLE PLACEMENT WOULD BE INEFFECTIVE OR WOULD INTERFERE WITH THE SAFE OPERATION OF TRAFFIC.
4. BARRIER VEHICLES ARE NOT REQUIRED FOR MILLING AND/OR PAVING OPERATIONS, BUT THE STANDARD LONGITUDINAL BUFFER SPACE (TABLE 6C-2) SHALL BE PROVIDED.
5. BARRIER VEHICLES ARE NOT REQUIRED FOR FLAGGING OPERATIONS.

TABLE NY1-B SHADOW VEHICLE USE REQUIREMENTS (MOBILE CLOSURES ¹)				
CLOSURE TYPE	EXPOSURE CONDITION	USE REQUIREMENTS		
		FREEWAY	NON-FREEWAY (PRECONSTRUCTION POSTED SPEED LIMIT)	
			≥ 45 MPH	35-40 MPH ≤ 30 MPH
LANE CLOSURE	WHEN ANY WORKERS, VEHICLES, OR OTHER HAZARD IS EXPOSED TO TRAFFIC	REQUIRED ^{2,4}	REQUIRED ^{2,4}	REQUIRED ^{2,4} REQUIRED ^{3,4}
SHOULDER CLOSURE	WHEN ANY WORKERS, VEHICLES, OR OTHER HAZARD IS EXPOSED TO TRAFFIC	REQUIRED ^{2,4}	REQUIRED ^{2,4}	REQUIRED ^{3,4} REQUIRED ^{3,4}

1. A MOBILE CLOSURE SHALL BE USED FOR ANY WORK ACTIVITY THAT MOVES CONTINUOUSLY OR INTERMITTENTLY ALONG THE TRAVELED WAY OR SHOULDER SLOWER THAN THE PREVAILING SPEED OF TRAFFIC. CHANNELIZING DEVICES ARE NOT USED FOR MOBILE CLOSURES.
2. SHADOW VEHICLES SHALL BE EQUIPPED WITH AN APPROVED REAR MOUNTED ATTENUATOR (TRUCK-MOUNTED OR TRAILER MOUNTED) FOR THE FOLLOWING MOBILE CLOSURES: LANE CLOSURES ON FREEWAYS, LANE CLOSURES ON NON-FREEWAY ROADWAYS HAVING A PRE-CONSTRUCTION POSTED SPEED LIMIT OF 35 MPH OR MORE, SHOULDER CLOSURES ON FREEWAYS, AND SHOULDER CLOSURES ON NON-FREEWAY ROADWAYS HAVING A PRE-CONSTRUCTION SPEED LIMIT OF 45 MPH OR MORE.
3. FOR MOBILE LANE CLOSURES ON NON-FREEWAY ROADWAYS HAVING A PRE-CONSTRUCTION POSTED SPEED LIMIT OF 30 MPH OR LESS AND MOBILE SHOULDER CLOSURES ON NON-FREEWAY ROADWAYS HAVING A PRE-CONSTRUCTION SPEED LIMIT OF 40 MPH OR LESS, SHADOW VEHICLES ARE NOT REQUIRED TO BE EQUIPPED WITH A REAR MOUNTED ATTENUATOR.
4. A SHADOW VEHICLE IS USED TO PROTECT EXPOSED WORKERS (ON FOOT OR IN A VEHICLE) AND SHALL BE REQUIRED FOR ALL MOBILE CLOSURES. SHADOW VEHICLE REQUIREMENTS SHALL INCLUDE PROVIDING A SEPARATE SHADOW VEHICLE FOR EACH CLOSED LANE AND EACH CLOSED SHOULDER 8 FEET OR GREATER IN WIDTH. ADDITIONAL SHADOW VEHICLES MAY BE REQUIRED TO PROMOTE THE SAFE OPERATION OF TRAFFIC AND THE INCREASED PROTECTION OF EXPOSED WORKERS, AS DIRECTED BY THE ENGINEER.

TABLE NY2-A PLACEMENT DISTANCE FOR BARRIER VEHICLES				
PRECONSTRUCTION POSTED SPEED LIMIT (MPH)	PLACEMENT DISTANCE (FT)			
	BARRIER VEHICLES			
	18000 LBS.	24000 LBS.		
	MINIMUM	MAXIMUM	MINIMUM	MAXIMUM
> 55	100 FT	200 FT	100 FT	200 FT
45 - 55	100 FT	200 FT	80 FT	160 FT
< 45	80 FT	160 FT	50 FT	100 FT

AS DEFINED IN NYSDOT STANDARD SPECIFICATION 619:

BARRIER VEHICLE: VEHICLE USED FOR STATIONARY SHOULDER CLOSURES, LANE CLOSURES AND OTHER STATIONARY WORK ZONES.

MINIMUM DISTANCE SHOWN REFLECTS THE ACTUAL ROLL AHEAD DISTANCE FROM MANUFACTURER.

TABLE NY2-B PLACEMENT DISTANCE FOR SHADOW VEHICLES				
PRECONSTRUCTION POSTED SPEED LIMIT (MPH)	PLACEMENT DISTANCE (FT)			
	SHADOW VEHICLES			
	18000 LBS.	24000 LBS.		
	MINIMUM	MAXIMUM	MINIMUM	MAXIMUM
> 55	230 FT	325 FT	180 FT	280 FT
45 - 55	180 FT	280 FT	150 FT	250 FT
< 45	100 FT	200 FT	100 FT	200 FT

AS DEFINED IN NYSDOT STANDARD SPECIFICATION 619:

SHADOW VEHICLE: VEHICLE USED FOR MOBILE OR SHORT DURATION WORK OPERATIONS.

MINIMUM DISTANCE SHOWN REFLECTS THE ACTUAL ROLL AHEAD DISTANCE FROM MANUFACTURER.

TABLE NY6H-3 ADVANCE WARNING SIGN SPACING					
ROAD TYPE	DISTANCE BETWEEN SIGNS			SIGN LEGEND	
	A (FT)	B (FT)	C (FT)	XX	YY
URBAN (130 MPH*)	100	100	100	AHEAD	AHEAD
URBAN (35-40 MPH*)	200	200	200	AHEAD	AHEAD
URBAN (w/45 MPH*)	350	350	350	1000 FT	AHEAD
RURAL	500	500	500	1500 FT	1000 FT
EXPRESSWAY/FREEWAY	1,000	1,500	2,640	1 MILE	1/2 MILE

* PRECONSTRUCTION POSTED SPEED LIMIT

URBAN:
ANY AREA EXHIBITING AT LEAST TWO OF THE FOLLOWING CHARACTERISTICS: SIDEWALKS, BICYCLE USAGE, CURBING, CLOSED DRAINAGE SYSTEMS, DRIVEWAY DENSITIES GREATER THAN 24 DRIVEWAYS PER MILE, MINOR COMMERCIAL DRIVEWAY DENSITIES OF 10 DRIVEWAYS PER MILE OR GREATER, MAJOR COMMERCIAL DRIVEWAYS, NUMEROUS RIGHT-OF-WAY CONSTRAINTS, HIGH DENSITY OF CROSS STREETS, OPERATING SPEEDS OF 45 MPH OR LESS.

RURAL:
ANY AREA EXHIBITING NO MORE THAN ONE OF ABOVE CHARACTERISTICS.

EXPRESSWAY:
DIVIDED HIGHWAYS FOR THROUGH TRAFFIC WITH FULL OR PARTIAL CONTROL OF ACCESS AND GENERALLY WITH GRADE SEPARATIONS AT MAJOR CROSSROADS.

FREEWAY/INTERSTATE:
LOCAL OR INTERREGIONAL HIGH-SPEED, DIVIDED, HIGH-VOLUME FACILITIES WITH FULL OR PARTIAL CONTROL OF ACCESS.

THRUWAY WORK DURATION DEFINITIONS	
LONG-TERM STATIONARY	WORK THAT OCCUPIES A LOCATION MORE THAN 3 CONSECUTIVE DAYS.
INTERMEDIATE-TERM STATIONARY	WORK THAT OCCUPIES A LOCATION MORE THAN ONE DAYLIGHT PERIOD UP TO 3 CONSECUTIVE DAYS, OR NIGHTTIME WORK LASTING MORE THAN 1 HOUR.
SHORT-TERM STATIONARY	DAYTIME WORK THAT OCCUPIES A LOCATION WITHIN A SINGLE DAYLIGHT PERIOD.
SHORT DURATION	IS DAYTIME WORK THAT OCCUPIES A LOCATION UP TO 2 HOURS, OR NIGHTTIME WORK LASTING UP TO 1 HOUR.
MOBILE	IS WORK THAT MOVES INTERMITTENTLY OR CONTINUOUSLY.

TABLE 619-4 FLARE RATES FOR POSITIVE BARRIER						
TYPE OF POSITIVE BARRIER	PRECONSTRUCTION POSTED SPEED LIMIT					
	30 MPH	40 MPH	50 MPH	55 MPH	65 MPH	
TEMPORARY CONCRETE BARRIER	8:1	11:1	14:1	16:1	20:1	
BOX BEAM OR HEAVY POST CORRUGATED BEAM	7:1	9:1	11:1	12:1	15:1	


TABLE 6C-2 LONGITUDINAL BUFFER SPACE	
PRECONSTRUCTION POSTED SPEED LIMIT (MPH)	DISTANCE
25	155 FT
30	200 FT
35	250 FT
40	305 FT
45	360 FT
50	425 FT
55	495 FT
60	570 FT
65	645 FT

TABLE 6H-4 FORMULAS FOR DETERMINING TAPER LENGTHS											
SPEED LIMIT (S) (MPH)		TAPER LENGTH (L) (FEET)		L = TAPER LENGTH (FEET) W = WIDTH OF OFFSET (FEET) S = PRE-CONSTRUCTION POSTED SPEED LIMIT (MPH)							
40 MPH OR LESS		L = WS ² /60									
45 MPH OR MORE		L = WS									
STANDARD TAPER LENGTHS											
LATERAL SHIFT OF TRAFFIC FLOW PATH		WORK ZONE PRE-CONSTRUCTION POSTED SPEED LIMIT									
		25 MPH	30 MPH	35 MPH	40 MPH	45 MPH	50 MPH	55 MPH	60 MPH	65 MPH	70 MPH
4 FT	40 FT	60 FT	80 FT	105 FT	180 FT	200 FT	220 FT	240 FT	260 FT	280 FT	300 FT
5 FT	50 FT	75 FT	100 FT	135 FT	225 FT	250 FT	275 FT	300 FT	325 FT	350 FT	375 FT
6 FT	65 FT	90 FT	125 FT	160 FT	270 FT	300 FT	330 FT	360 FT	390 FT	420 FT	450 FT
7 FT	75 FT	105 FT	145 FT	185 FT	315 FT	350 FT	385 FT	420 FT	455 FT	490 FT	525 FT
8 FT	85 FT	120 FT	165 FT	215 FT	360 FT	400 FT	440 FT	480 FT	520 FT	560 FT	600 FT
9 FT	95 FT	135 FT	185 FT	240 FT	405 FT	450 FT	495 FT	540 FT	585 FT	630 FT	675 FT
10 FT	105 FT	150 FT	205 FT	265 FT	450 FT	500 FT	550 FT	600 FT	650 FT	700 FT	750 FT
11 FT	115 FT	165 FT	225 FT	295 FT	495 FT	550 FT	605 FT	660 FT	715 FT	770 FT	825 FT
12 FT	125 FT	180 FT	245 FT	320 FT	540 FT	600 FT	660 FT	720 FT	780 FT	840 FT	900 FT


WORK ZONE TRAFFIC CONTROL LEGEND	
SYMBOL	DESCRIPTION
	ARROW PANEL
	ARROW PANEL, CAUTION MODE
	ARROW PANEL SUPPORT OR TRAILER
	CHANGEABLE MESSAGE SIGN (PWS)
	CHANNELIZING DEVICE
	CRASH CUSHION/TEMPORARY IMPACT ATTENUATOR
	DIRECTION OF TEMPORARY TRAFFIC DETOUR
	DIRECTION OF TRAFFIC
	FLAGGER
	FLAG TREE
	LUMINAIRE
	PAVEMENT MARKINGS THAT SHALL BE REMOVED FOR A LONG TERM PROJECT
	SIGN, TEMPORARY
	TEMPORARY BARRIER
	TEMPORARY BARRIER WITH WARNING LIGHTS
	TRAFFIC OR PEDESTRIAN SIGNAL
	TYPE III BARRICADE
	WARNING LIGHTS
	WORK SPACE
	WORK VEHICLE
	WORK VEHICLE W/ TRUCK MOUNTED ATTENUATOR
	TEMP/INTERIM PAVEMENT MARKING

TABLE 6C-3 TAPER LENGTH CRITERIA FOR WORK ZONES	
TYPE OF TAPER	TAPER LENGTH (L)
MERGING TAPER	L
SHIFTING TAPER	L/2
SHOULDER TAPER	L/3
ONE-LANE, TWO-WAY TRAFFIC TAPER	100 FT MAXIMUM
DOWNSTREAM TAPER	100 FT PER LANE


U.S. CUSTOMARY STANDARD SHEET	
WORK ZONE TRAFFIC CONTROL TABLES AND LEGEND (DRAWING TL)	
APPROVED SEPTEMBER 21, 2016	ISSUED UNDER ET 16-001
/S/ PATRICK THOMPSON, P.E. DIRECTOR DESIGN SUPPORT SERVICES BUREAU	TA 619-01

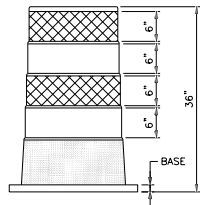


DRUM

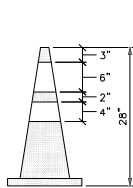


STANDARD CONE

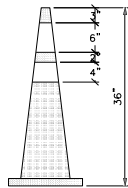


TALL CONE

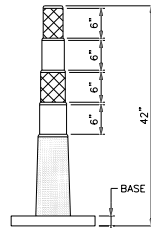


EXTRA TALL CONE

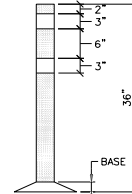


TUBULAR MARKER

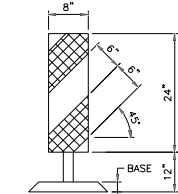

STANDARD
VERTICAL PANEL

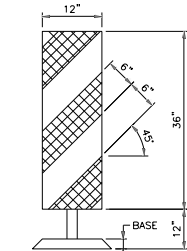

OVERSIZED
VERTICAL PANEL

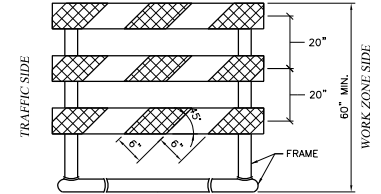

TYPE III BARRICADE

CHANNELIZING DEVICES

N.T.S.

GENERAL NOTES:

1. THE ENGINEER SHALL APPROVE THE CONDITION OF ALL TEMPORARY TRAFFIC CONTROL DEVICES PRIOR TO USE. THE ENGINEER SHALL ALSO REVIEW THE PROPOSED WORK ZONE TRAFFIC CONTROL PLAN FOR PRECISE DEVICE POSITIONING PRIOR TO INSTALLATION.
2. ALL SIGNS SHALL CONFORM TO THE MANUAL ON UNIFORM TRAFFIC CONTROL DEVICES (MUTCD). ALL CONSTRUCTION SIGN FACES ON RIGID PANELS SHALL CONFORM TO SECTION 730-05 - REFLECTIVE SHEETING.
3. EXISTING SPEED LIMIT SIGNS WITHIN THE WORK ZONE SHALL BE COMPLETELY COVERED TO AVOID CONFLICT WITH THE WORK ZONE SPEED LIMIT SIGNS.
4. WHEN A SPEED DISPLAY TRAILER IS DEPLOYED, IT MAY BE USED AS A SUBSTITUTE FOR THE SECOND "WORK ZONE/SPEED LIMIT 45" SIGN (G20-5AP/R2-1). THE UNIT SHALL BE PROVIDED IN ACCORDANCE WITH THE CONTRACT SPECIFICATIONS. WHEN NOT IN OPERATION, THE SPEED DISPLAY TRAILER SHALL BE REMOVED FROM THE WORK ZONE.
5. CHANNELIZING DEVICES SHALL CONFORM TO THE REQUIREMENTS OF THE MUTCD AND SECTION 729 OF THE STANDARD SPECIFICATIONS WITH THE EXCEPTION THAT SHEETING REQUIREMENTS SHALL BE AS SPECIFIED ON THIS DRAWING. CHANNELIZING DEVICE TYPE AND SPACING REQUIREMENTS SHALL BE IN ACCORDANCE WITH SECTION 619 OF THE STANDARD SPECIFICATIONS.
6. ARROW PANELS SHALL CONFORM TO SECTION 729-15 OF THE STANDARD SPECIFICATIONS. THE ADVANCE WARNING ARROW DISPLAY SHALL BE A FULL FLASHING ARROW ONLY. CHEVRONS AND SEQUENTIAL ARROW DISPLAYS SHALL NOT BE PERMITTED. THE CAUTION MODE DISPLAY SHALL BE FOUR FLASHING CORNERS. FLASHING BAR DISPLAYS SHALL NOT BE PERMITTED.
7. THERE SHALL BE NO WORK ACTIVITY, EQUIPMENT, VEHICLES AND/OR MATERIALS LOCATED WITHIN THE BUFFER SPACE. THE SAME SHALL ALSO APPLY TO THE SPACE BETWEEN THE BARRIER VEHICLE(S) AND THE ACTIVE WORK AREA (BARRIER VEHICLE PLACEMENT DISTANCE).
8. THE REAR FACE OF A TRUCK MOUNTED ATTENUATOR DEVICE, WHEN IN THE HORIZONTAL OR OPERATING POSITION (PROTECTIVE MODE), SHALL BE MARKED WITH 4-INCH WIDE NON-REFLECTIVE BLACK STRIPES ON HIGH RETROREFLECTIVE YELLOW SHEETING IN AN UPWARD POINTING V-SHAPED (INVERTED V) STRIPING PATTERN. REFLECTIVE SHEETING SHALL CONFORM TO 730-05 REFLECTIVE SHEETING ASTM TYPE I (CLASS A), ASTM TYPE III (CLASS B) OR HIGHER. REAR FACE OF ATTENUATOR DEVICE SHALL BE CLEAR OF ANY OBSTRUCTIONS AND NOT USED FOR MOUNTING OF ANY TEMPORARY SIGNING, INCLUDING REQUIRED CONSTRUCTION SIGNS

CHANNELIZING DEVICE

LEGEND

-  WHITE RETROREFLECTORIZED SHEETING, ASTM TYPE XI (AASHTO TYPE D, NYSDOT CLASS A)
-  ORANGE REFLECTORIZED SHEETING, ASTM TYPE XI (AASHTO TYPE D, NYSDOT CLASS A)
-  NON-REFLECTORIZED ORANGE



Thruway
Authority

U.S. CUSTOMARY STANDARD SHEET


GENERAL WZTC NOTES
AND CHANNELIZING DEVICES
(DRAWING GWZN)

APPROVED OCTOBER 1, 2021

/S/ PATRICK THOMPSON, P.E.
DIRECTOR DESIGN SUPPORT
SERVICES BUREAU

ISSUED UNDER DB 21-001

TA 619-02

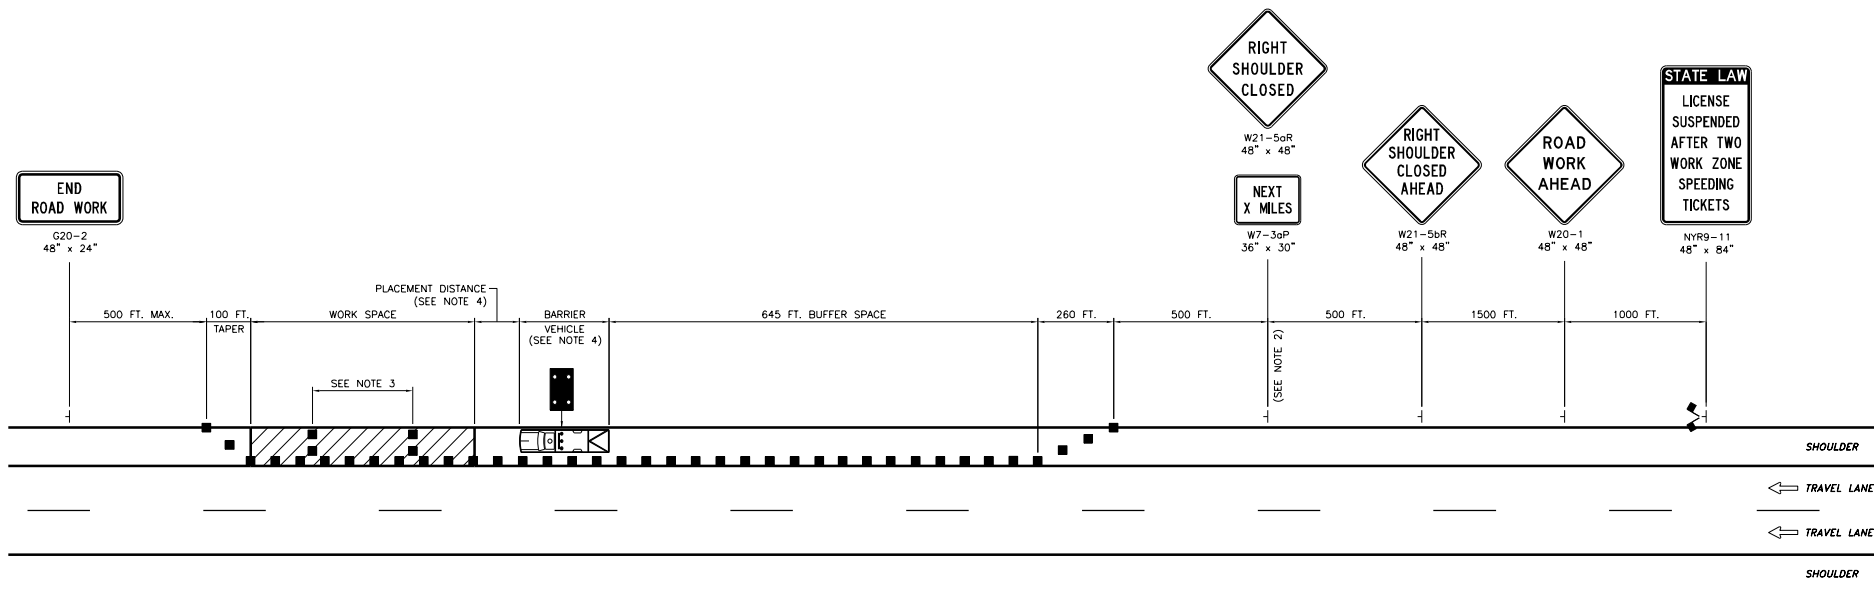


WORK ZONE TRAFFIC CONTROL PLAN

N.T.S.

NOTES:


1. THE PLAN SHOWN IS FOR A SHORT- OR INTERMEDIATE-TERM STATIONARY RIGHT SHOULDER CLOSURE. FOR A SHORT- OR INTERMEDIATE-TERM STATIONARY LEFT SHOULDER CLOSURE, SUBSTITUTE "LEFT SHOULDER CLOSED AHEAD" SIGN (W21-5bL) FOR THE "RIGHT SHOULDER CLOSED AHEAD" SIGN (W21-50R) AND "LEFT SHOULDER CLOSED" SIGN (W21-50L) FOR THE "RIGHT SHOULDER CLOSED" SIGN (W21-50R). THE SHORT- OR INTERMEDIATE-TERM STATIONARY LEFT SHOULDER CLOSURE PLAN SHALL BE THE MIRROR IMAGE OF THE PLAN SHOWN.
2. THE "NEXT X MILES" SUPPLEMENTAL SIGN (W7-30P) IS REQUIRED WHEN THE SHOULDER IS CLOSED FOR A DISTANCE GREATER THAN 2 MILES.
3. IN LONG WORK SPACES (1500 FEET AND GREATER) ON PAVED SHOULDERS HAVING A WIDTH OF 8 FEET OR GREATER, TWO DRUMS, TWO TALL CONES, OR TWO OVERSIZED VERTICAL PANELS SHALL BE PLACED TRANSVERSELY ACROSS THE CLOSED SHOULDER AT MAXIMUM INTERVALS OF 800 FEET. IN ADDITION, TWO DRUMS, TWO TALL CONES, OR TWO OVERSIZED VERTICAL PANELS SHALL BE SIMILARLY PLACED IN ADVANCE OF ANY TRANSVERSE DROP-OFF OF 1 1/2 INCHES OR GREATER.
4. THE BARRIER VEHICLE SHALL BE PROVIDED IN ACCORDANCE WITH SECTION 619 OF THE STANDARD SPECIFICATIONS. FOR BARRIER VEHICLE USE AND PLACEMENT REQUIREMENTS, SEE TABLES NY1-A AND NY2-A ON NYSTA STANDARD SHEET 619-01 - WORK ZONE TRAFFIC CONTROL TABLES AND LEGEND. THE BARRIER VEHICLE SHALL BE LOCATED COMPLETELY ON THE SHOULDER.

	Thruway Authority
U.S. CUSTOMARY STANDARD SHEET	
SHOULDER CLOSURE SHORT OR INTERMEDIATE TERM STATIONARY (DRAWING SC)	
APPROVED SEPTEMBER 1, 2018	ISSUED UNDER EI 18-003
/S/ PATRICK THOMPSON, P.E. DIRECTOR DESIGN SUPPORT SERVICES BUREAU	TA 619-03

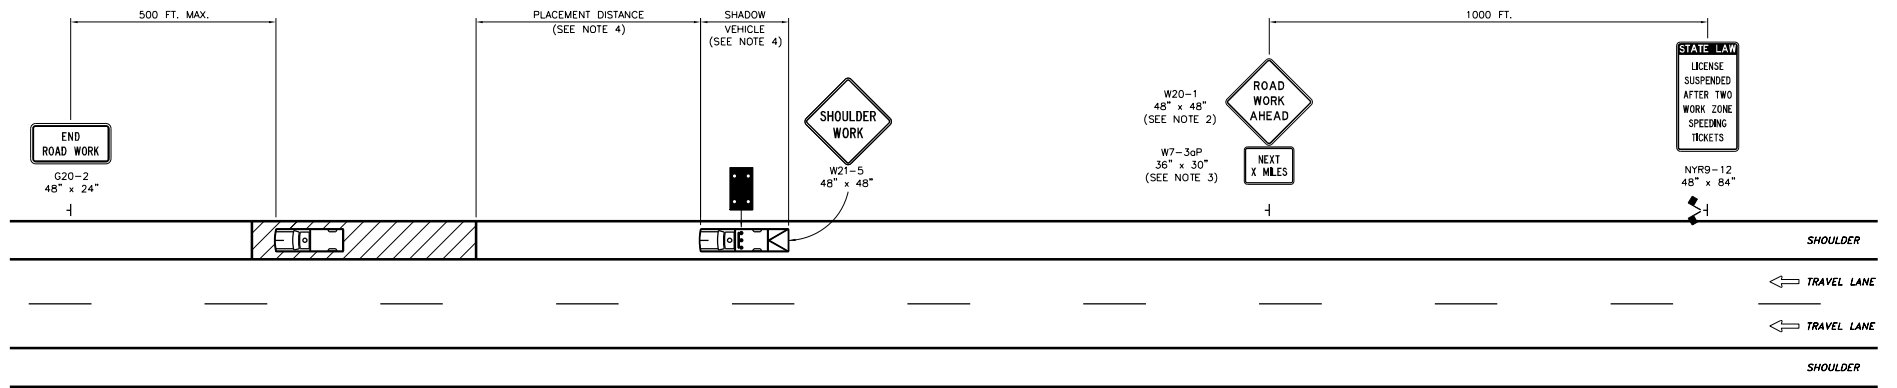

SHORT-DURATION STATIONARY OR MOBILE SHOULDER CLOSURE
(MULTIPLE WORK LOCATIONS)

N.T.S.

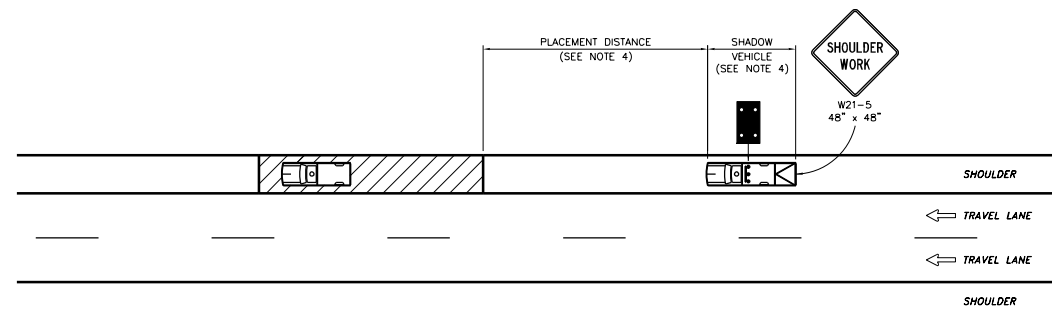

MOBILE OPERATION ON SHOULDER

N.T.S.

NOTES:

1. THE PLANS SHOWN ARE FOR SHORT-DURATION STATIONARY WORK OR MOBILE OPERATIONS ON THE RIGHT SHOULDER. THE LEFT SHOULDER PLANS SHALL BE THE MIRROR IMAGE OF THOSE SHOWN.
2. IN SITUATIONS WHERE MULTIPLE WORK LOCATIONS WITHIN A LIMITED DISTANCE MAKE IT PRACTICAL TO PLACE STATIONARY SIGNS, THE DISTANCE BETWEEN THE ADVANCE WARNING SIGN AND THE WORK SHALL NOT EXCEED 5 MILES.
3. IN SITUATIONS WHERE THE DISTANCE BETWEEN THE ADVANCE WARNING SIGNS AND THE WORK IS 2 MILES TO 5 MILES, THE "NEXT X MILES" SUPPLEMENTAL SIGN (W7-30P) SHALL BE USED WITH THE "ROAD WORK AHEAD" SIGN (W20-1).
4. THE SHADOW VEHICLE SHALL BE PROVIDED IN ACCORDANCE WITH SECTION 619 OF THE STANDARD SPECIFICATIONS. FOR SHADOW VEHICLE USE AND PLACEMENT REQUIREMENTS, SEE TABLES NY1-B AND NY2-B ON NYSTA STANDARD SHEET 619-01 - WORK ZONE TRAFFIC CONTROL TABLES AND LEGEND. THE SHADOW VEHICLE SHALL BE LOCATED COMPLETELY ON THE SHOULDER.



Thruway
Authority

U.S. CUSTOMARY STANDARD SHEET

SHOULDER CLOSURE
SHORT DURATION STATIONARY AND MOBILE
(DRAWING SCM)

APPROVED SEPTEMBER 1, 2018


/S/ PATRICK THOMPSON, P.E.
DIRECTOR DESIGN SUPPORT
SERVICES BUREAU

ISSUED UNDER E1 18-003


TA 619-04

LEGEND

- WORK SPACE
- CHANNELIZING DEVICE
- DIRECTION OF TRAFFIC
- TEMPORARY SIGN

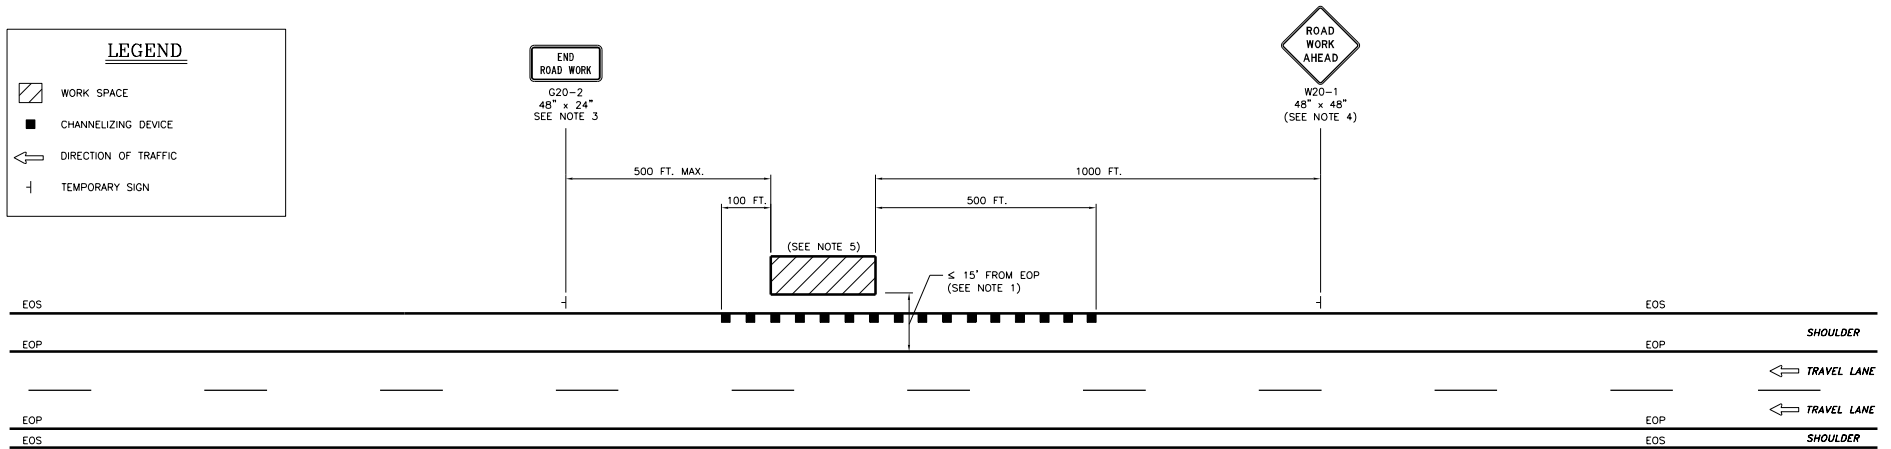

OPTION A WORK BEYOND SHOULDER N.T.S.

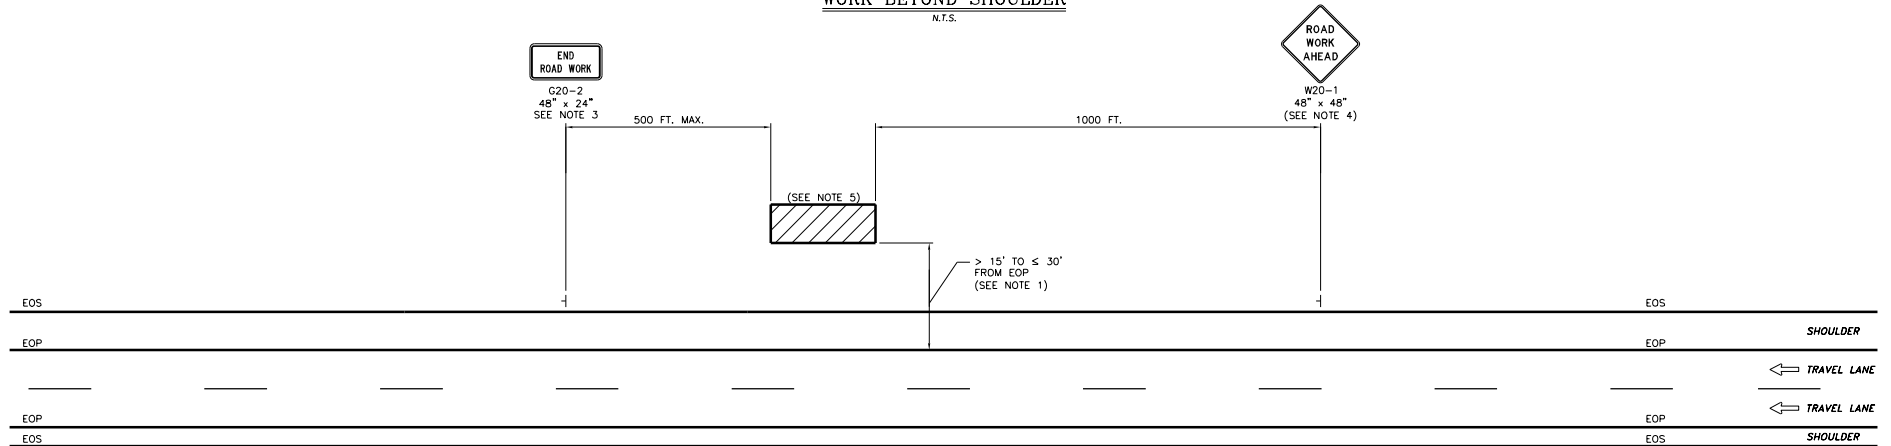

OPTION B WORK BEYOND SHOULDER N.T.S.

NOTES:

1. THE PLAN SHOWN IS FOR STATIONARY WORK BEING PERFORMED OFF THE ROADWAY (BEYOND THE SHOULDER, BUT WITHIN THE R.O.W.). NO TRAFFIC CONTROL IS REQUIRED WHERE THE WORK SPACE IS BEHIND A BARRIER OR CONFINED TO AN AREA MORE THAN 30' FROM THE EDGE OF TRAVEL WAY.
2. WHEN THE WORK SPACE IS IN THE MEDIAN AND AN ADVANCE "ROAD WORK AHEAD" SIGN IS REQUIRED, THE SIGN SHALL BE PLACED ON THE LEFT SIDE OF THE DIRECTIONAL ROADWAY.
3. THE "END ROAD WORK" SIGN IS OPTIONAL IF THE WORK DURATION IS TWO HOURS OR LESS.
4. A "SHOULDER WORK" W21-5 (48" x 48") MAY BE SUBSTITUTED FOR THE "ROAD WORK AHEAD" SIGN.
5. DURING NON-WORKING HOURS, ALL EQUIPMENT AND MATERIALS SHALL BE STORED AT LEAST THIRTY (30) FEET FROM THE EDGE OF PAVEMENT (BOTH MAINLINE AND RAMPS) OR BE PROTECTED BY A PHYSICAL BARRIER AS APPROVED BY THE ENGINEER.



Thruway
Authority

U.S. CUSTOMARY STANDARD SHEET

WORK BEYOND SHOULDER
(DRAWING WBS)

APPROVED NOVEMBER 1, 2018

ISSUED UNDER DB 18-005

/s/ PATRICK THOMPSON, P.E.
DIRECTOR DESIGN SUPPORT
SERVICES BUREAU

TA 619-06